




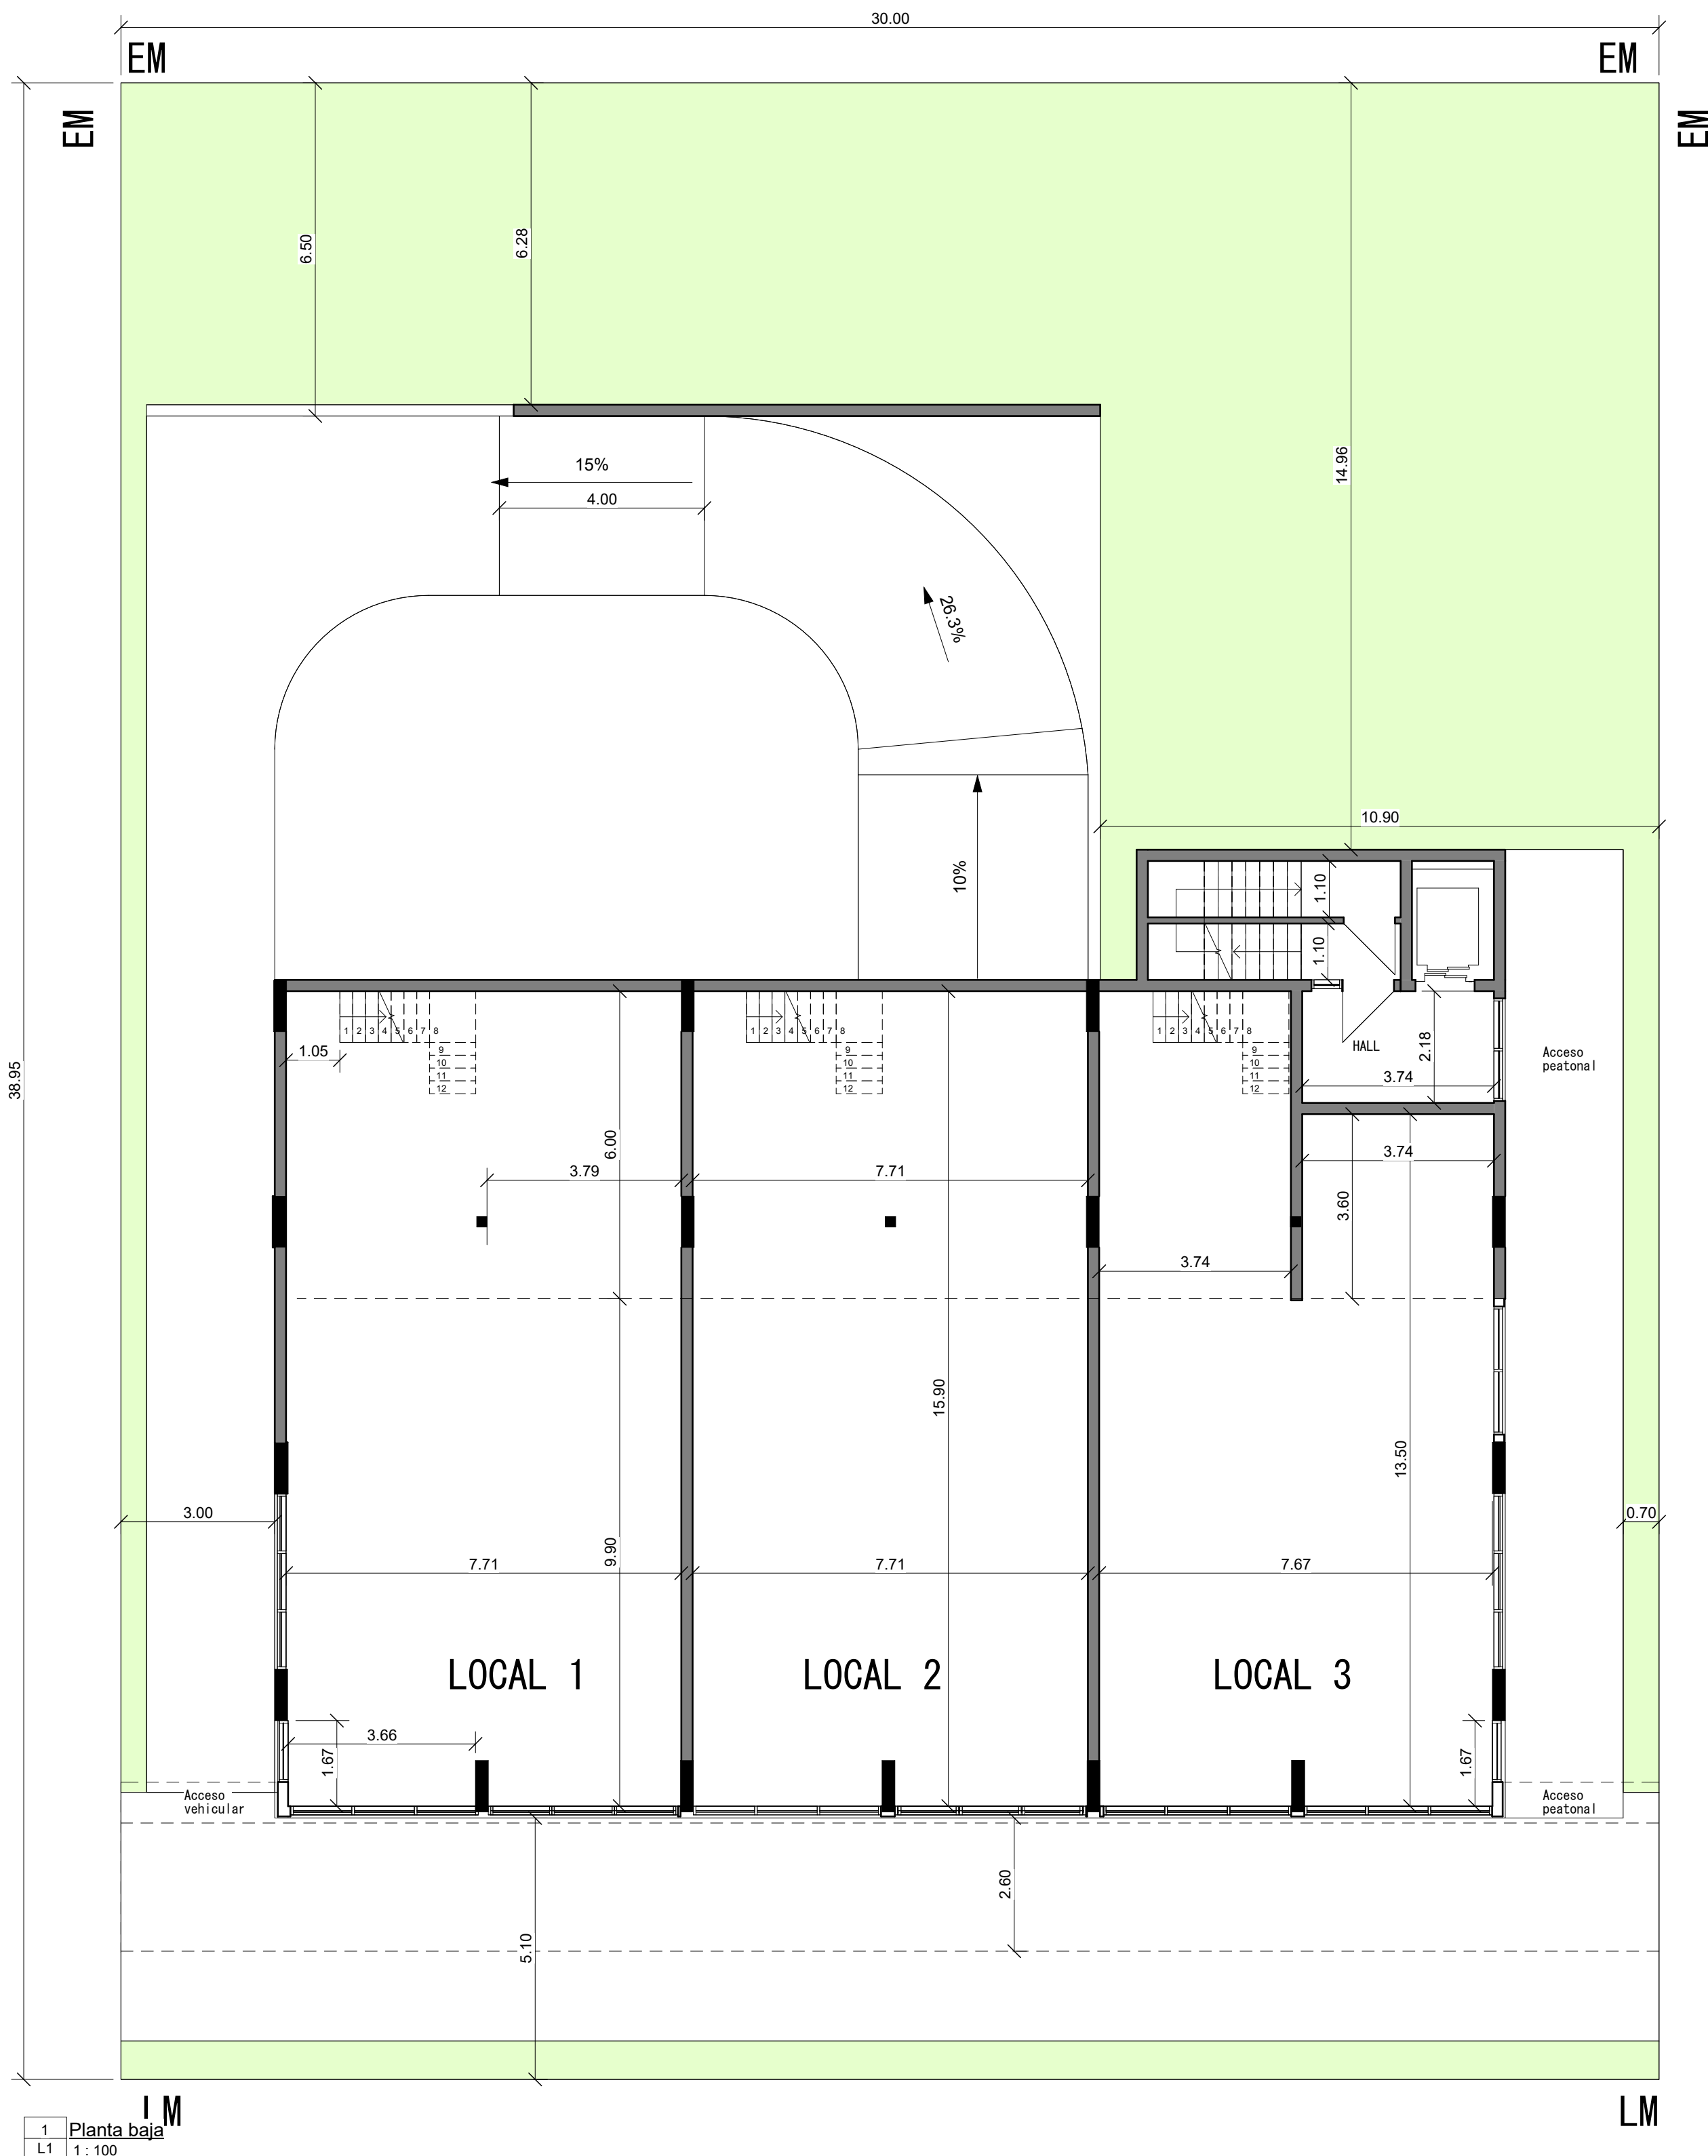




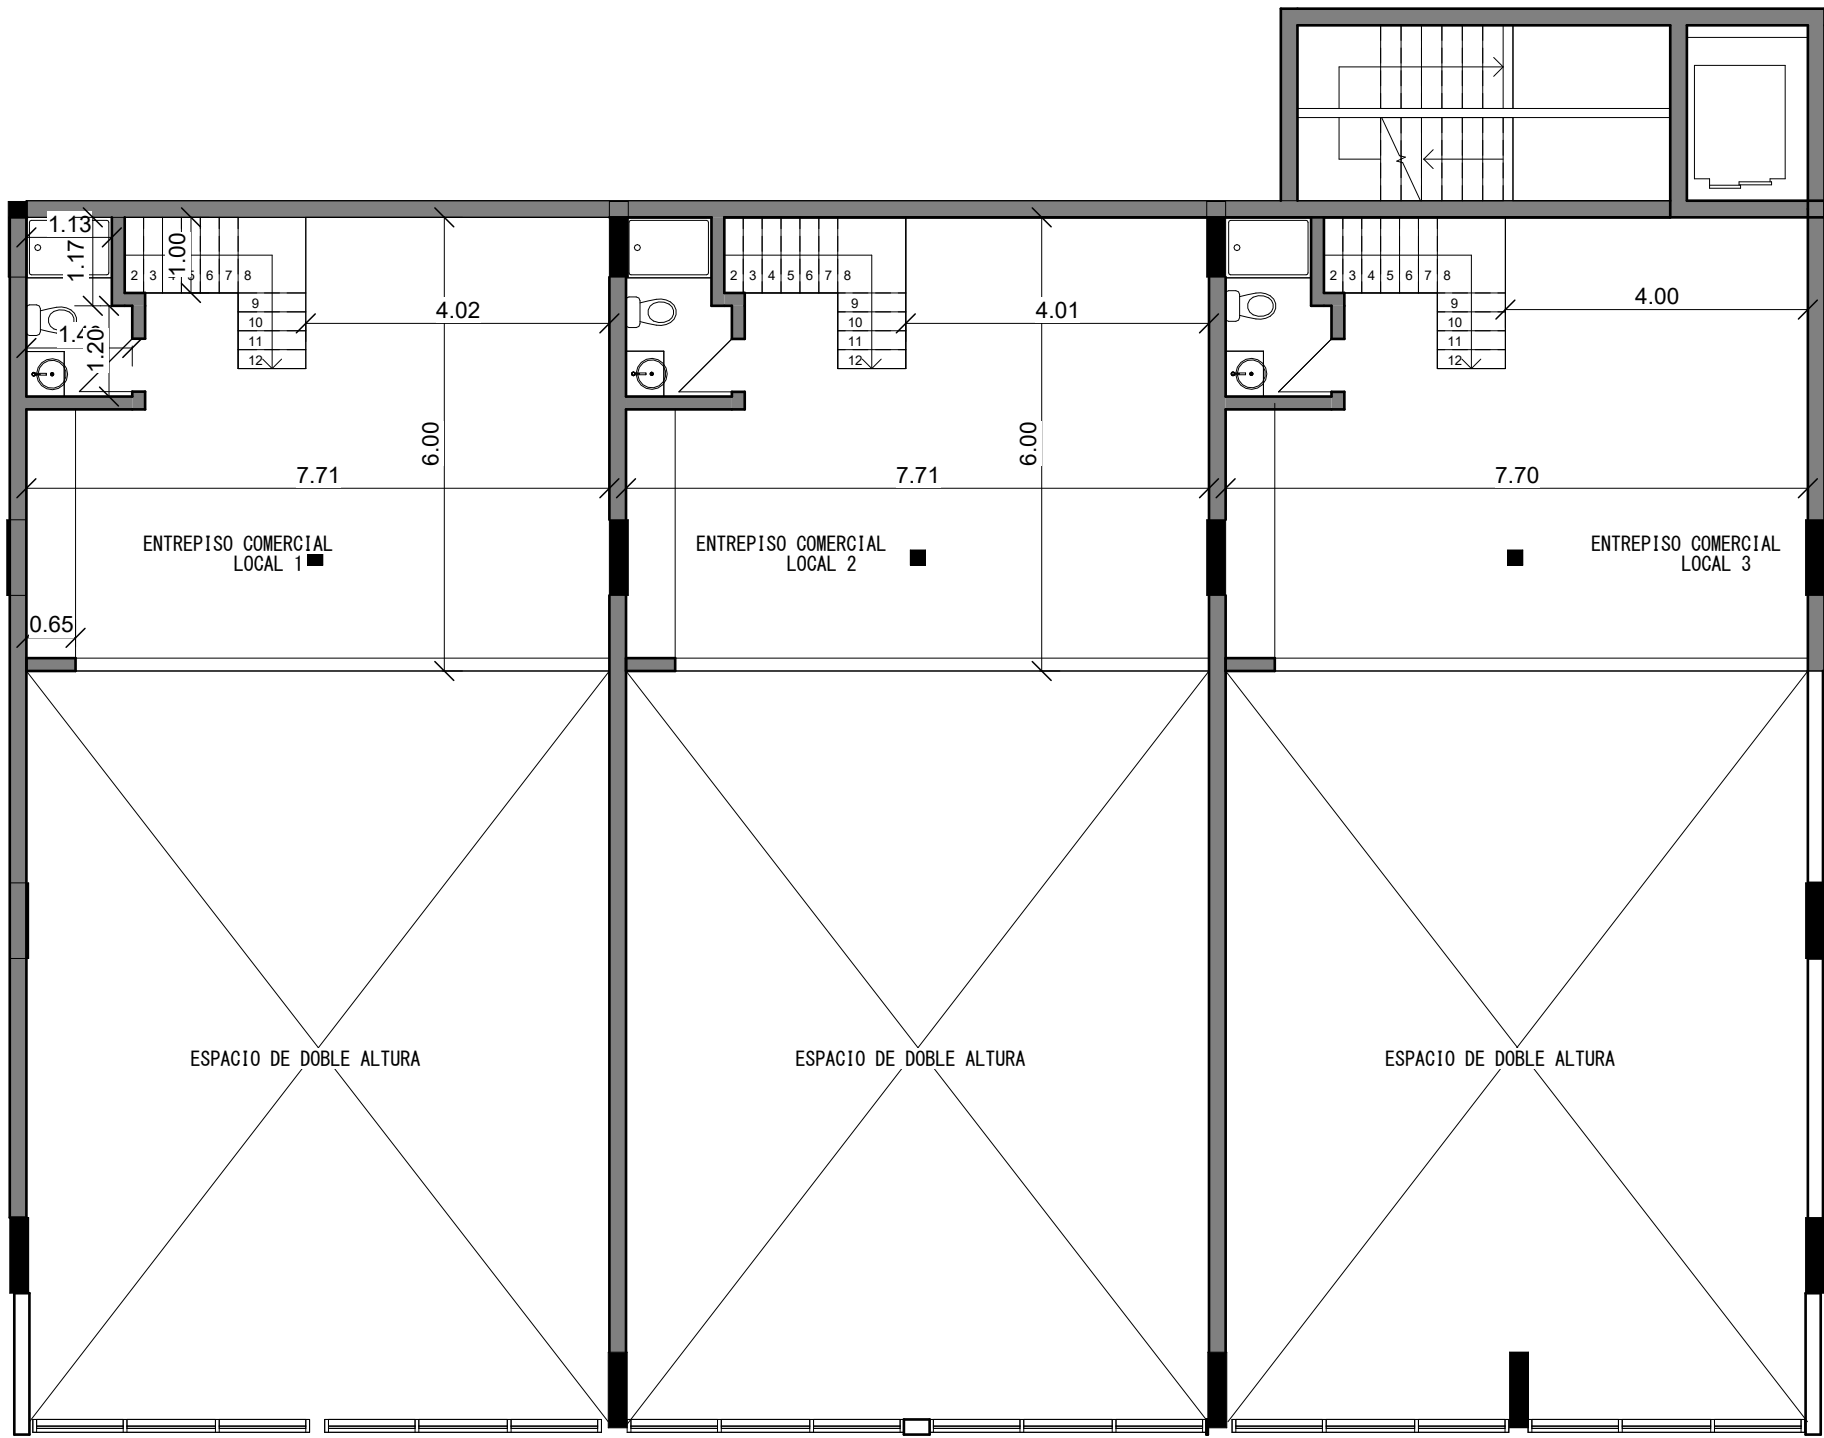

1	Entrepiso
L02	1 : 100

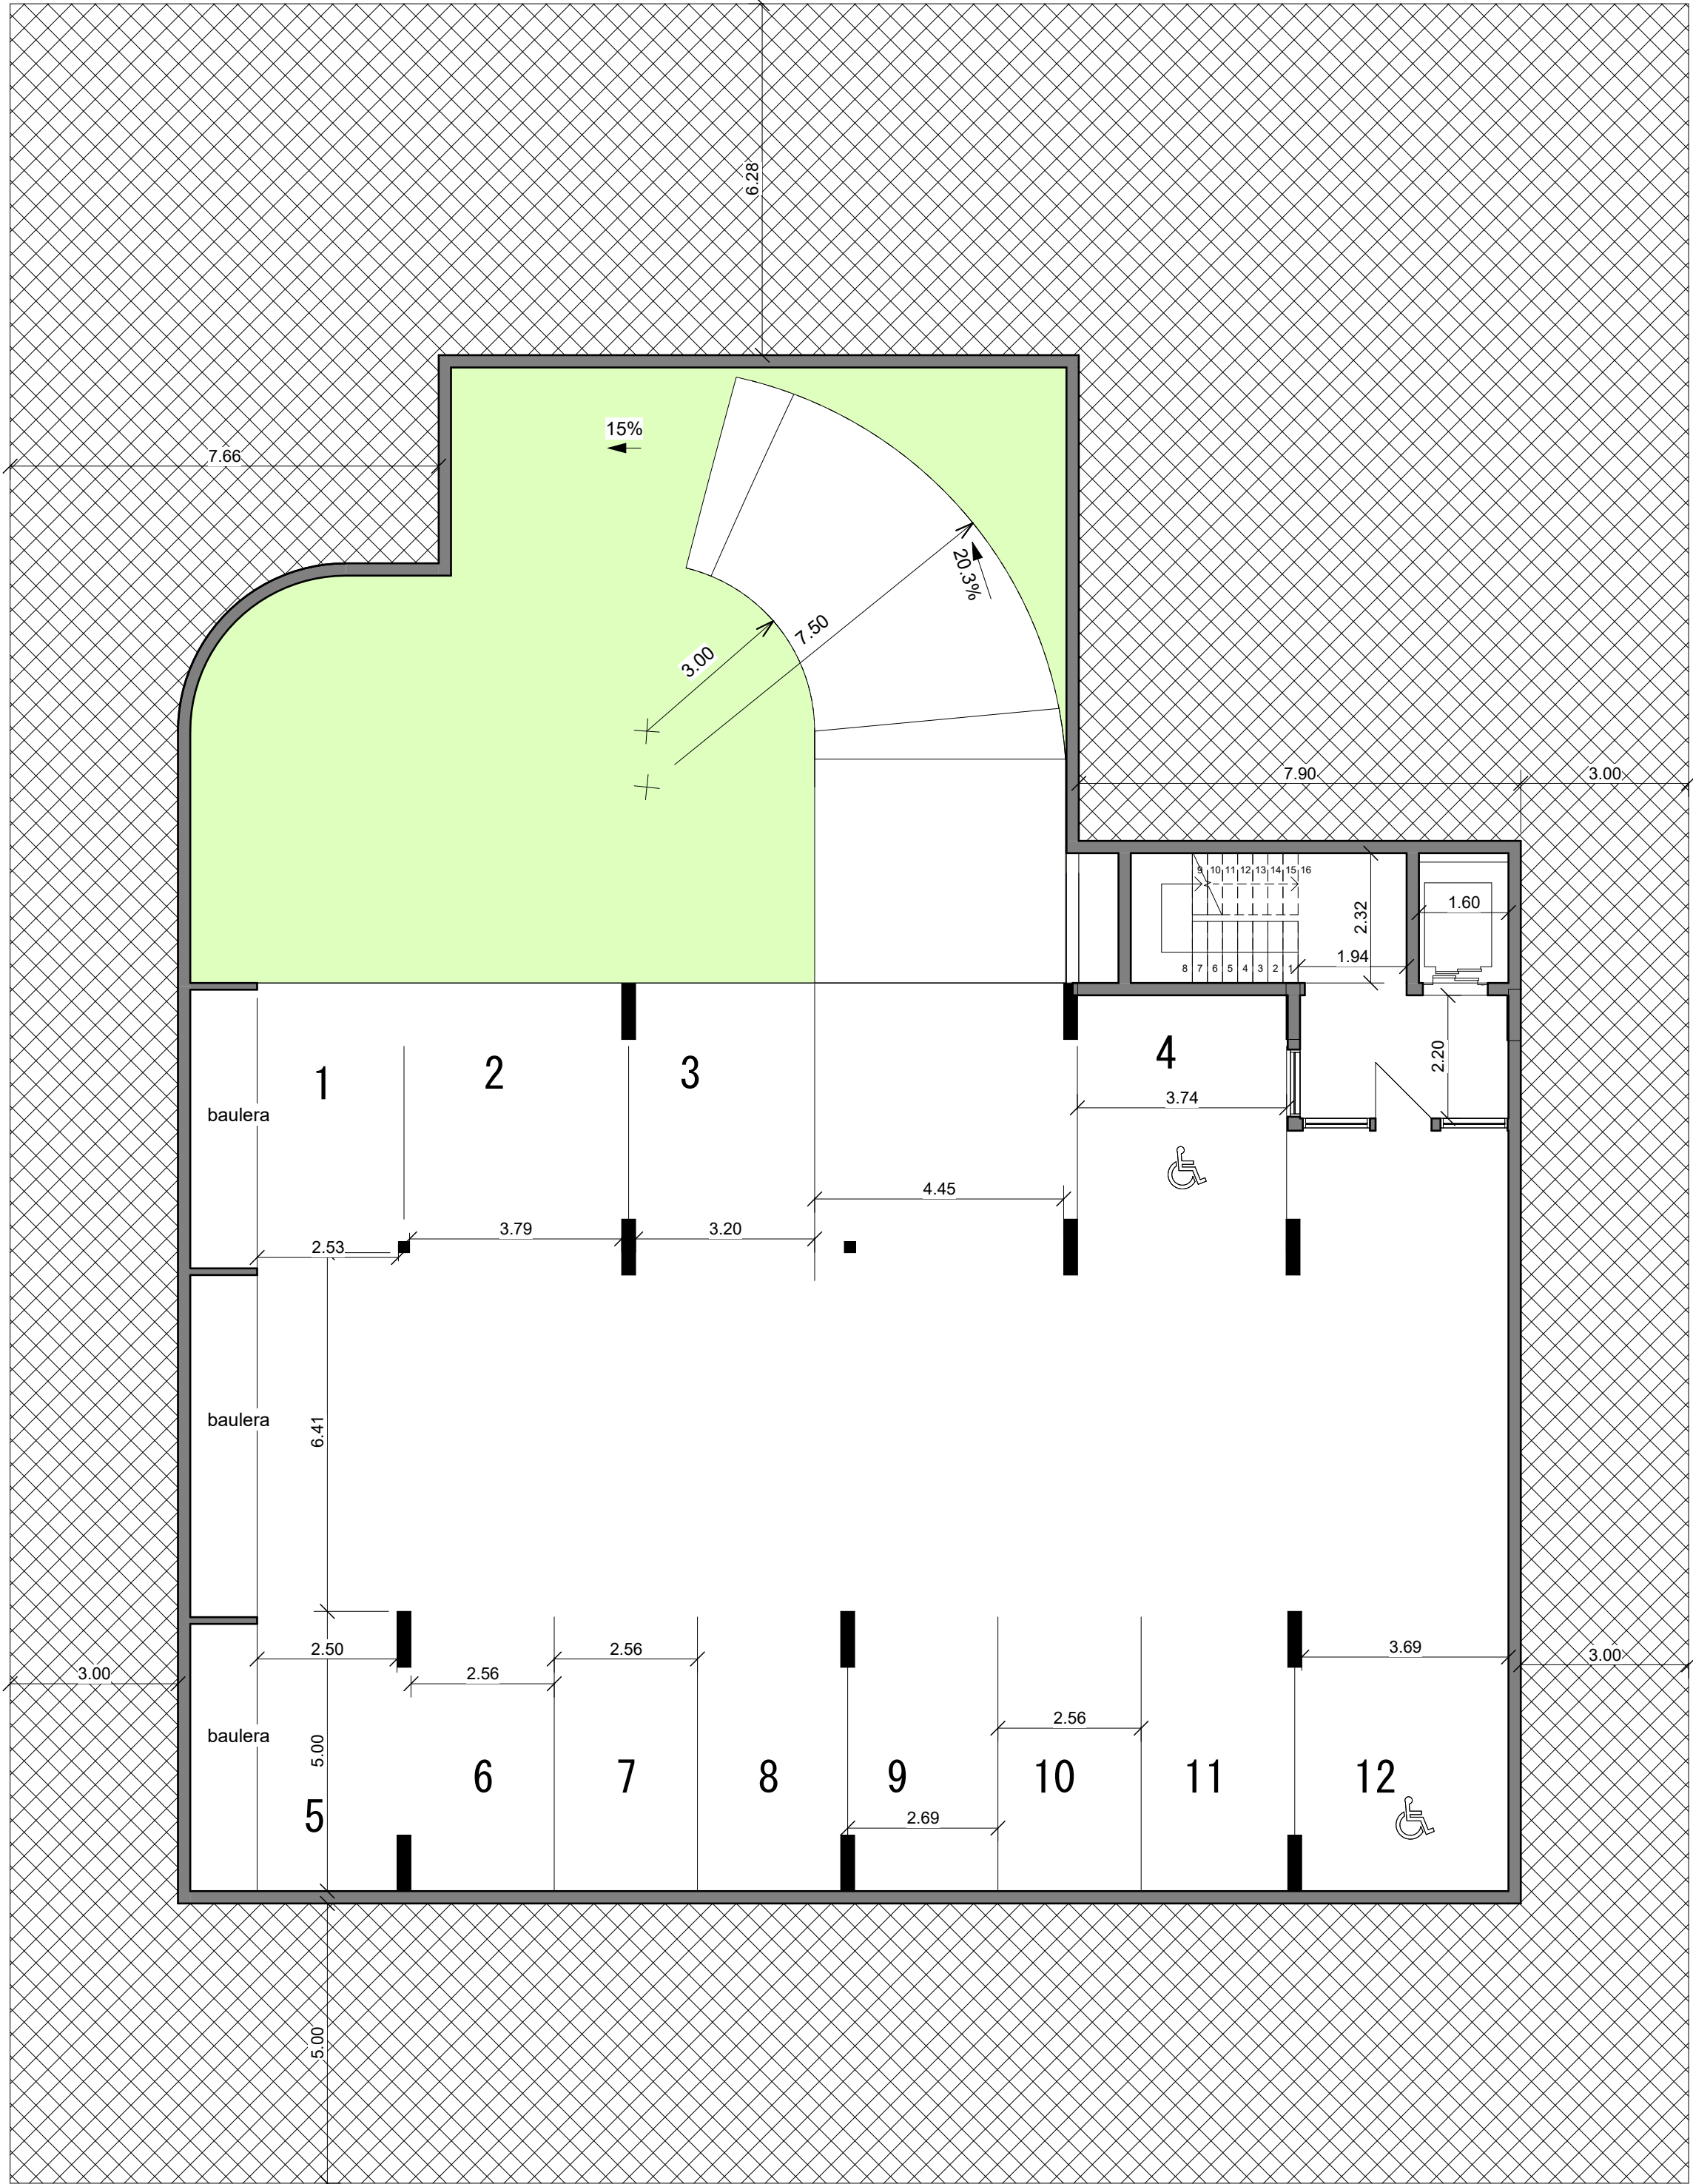

1 SUBSUELO
L03 1 : 100

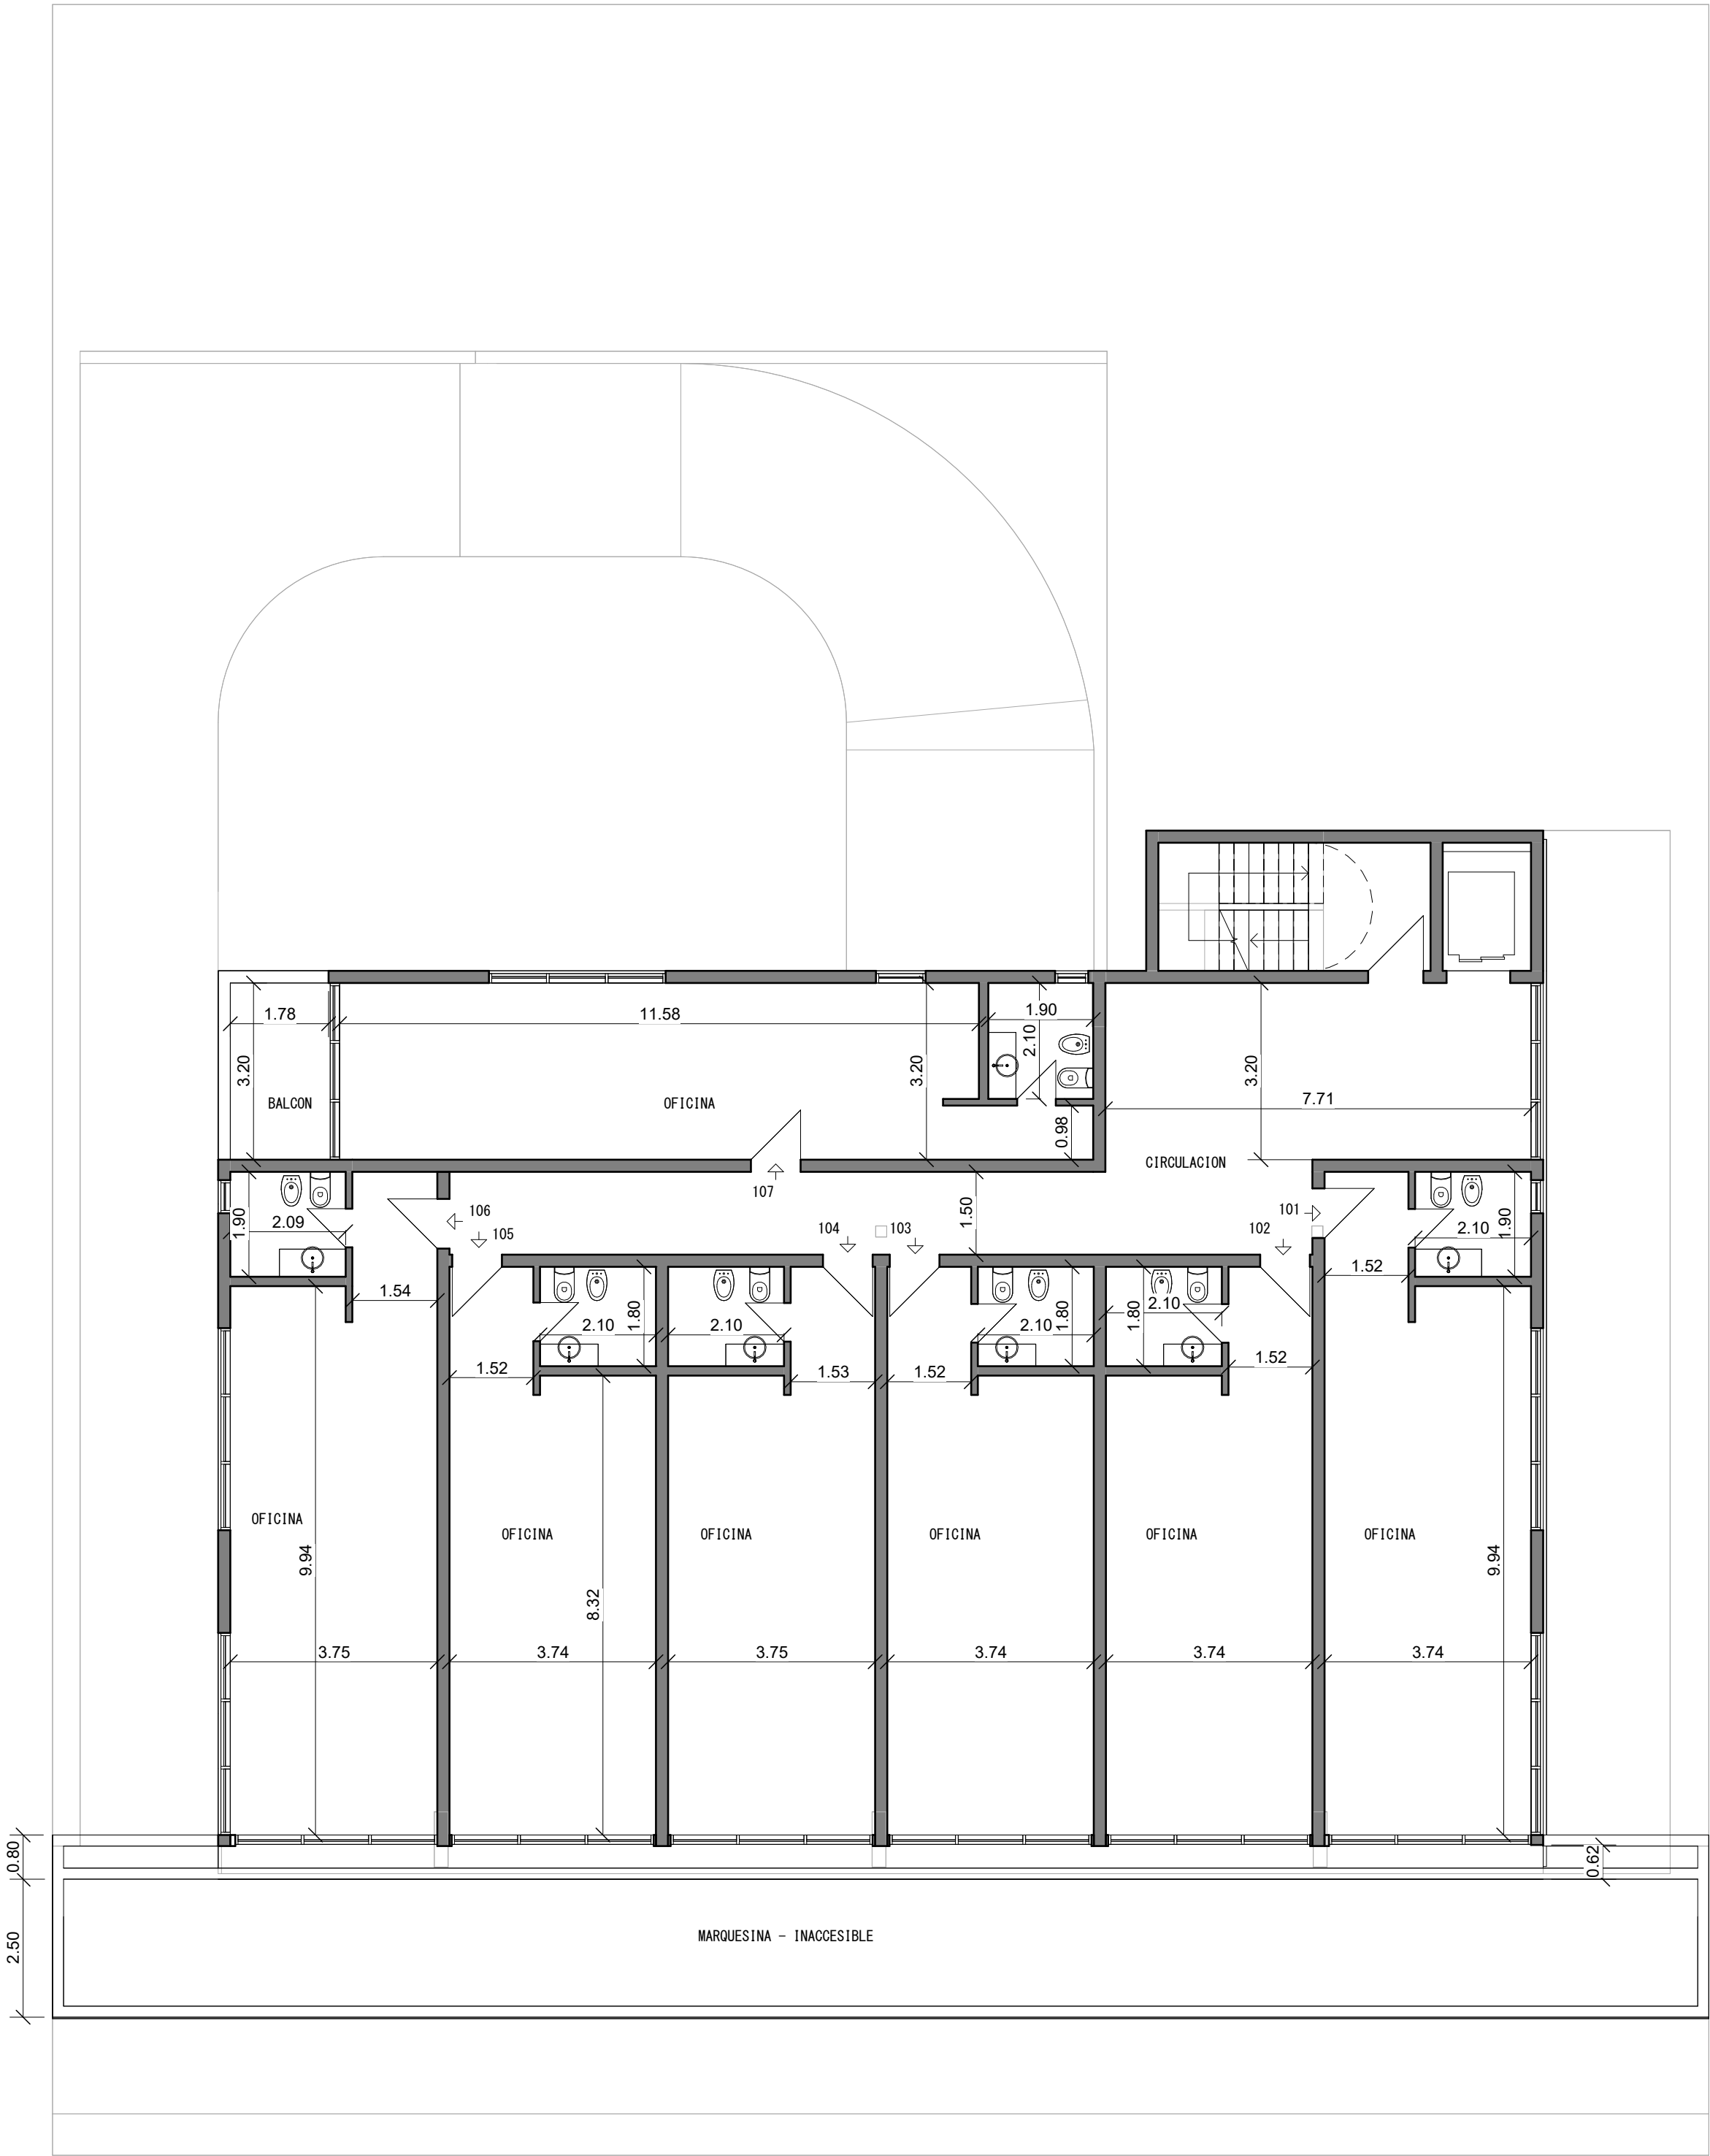

1 Piso 1
L04 1 : 100

OBRA SANTOS CHOQUE
2 lotes


Plano
PISO 1

L04

Fecha
04 JUNIO 2026

Escala
1 : 100

fmaarquitecto
2236 210 707 - (7167) Pinamar - Buenos Aires
fmaarquitecto23@gmail.com

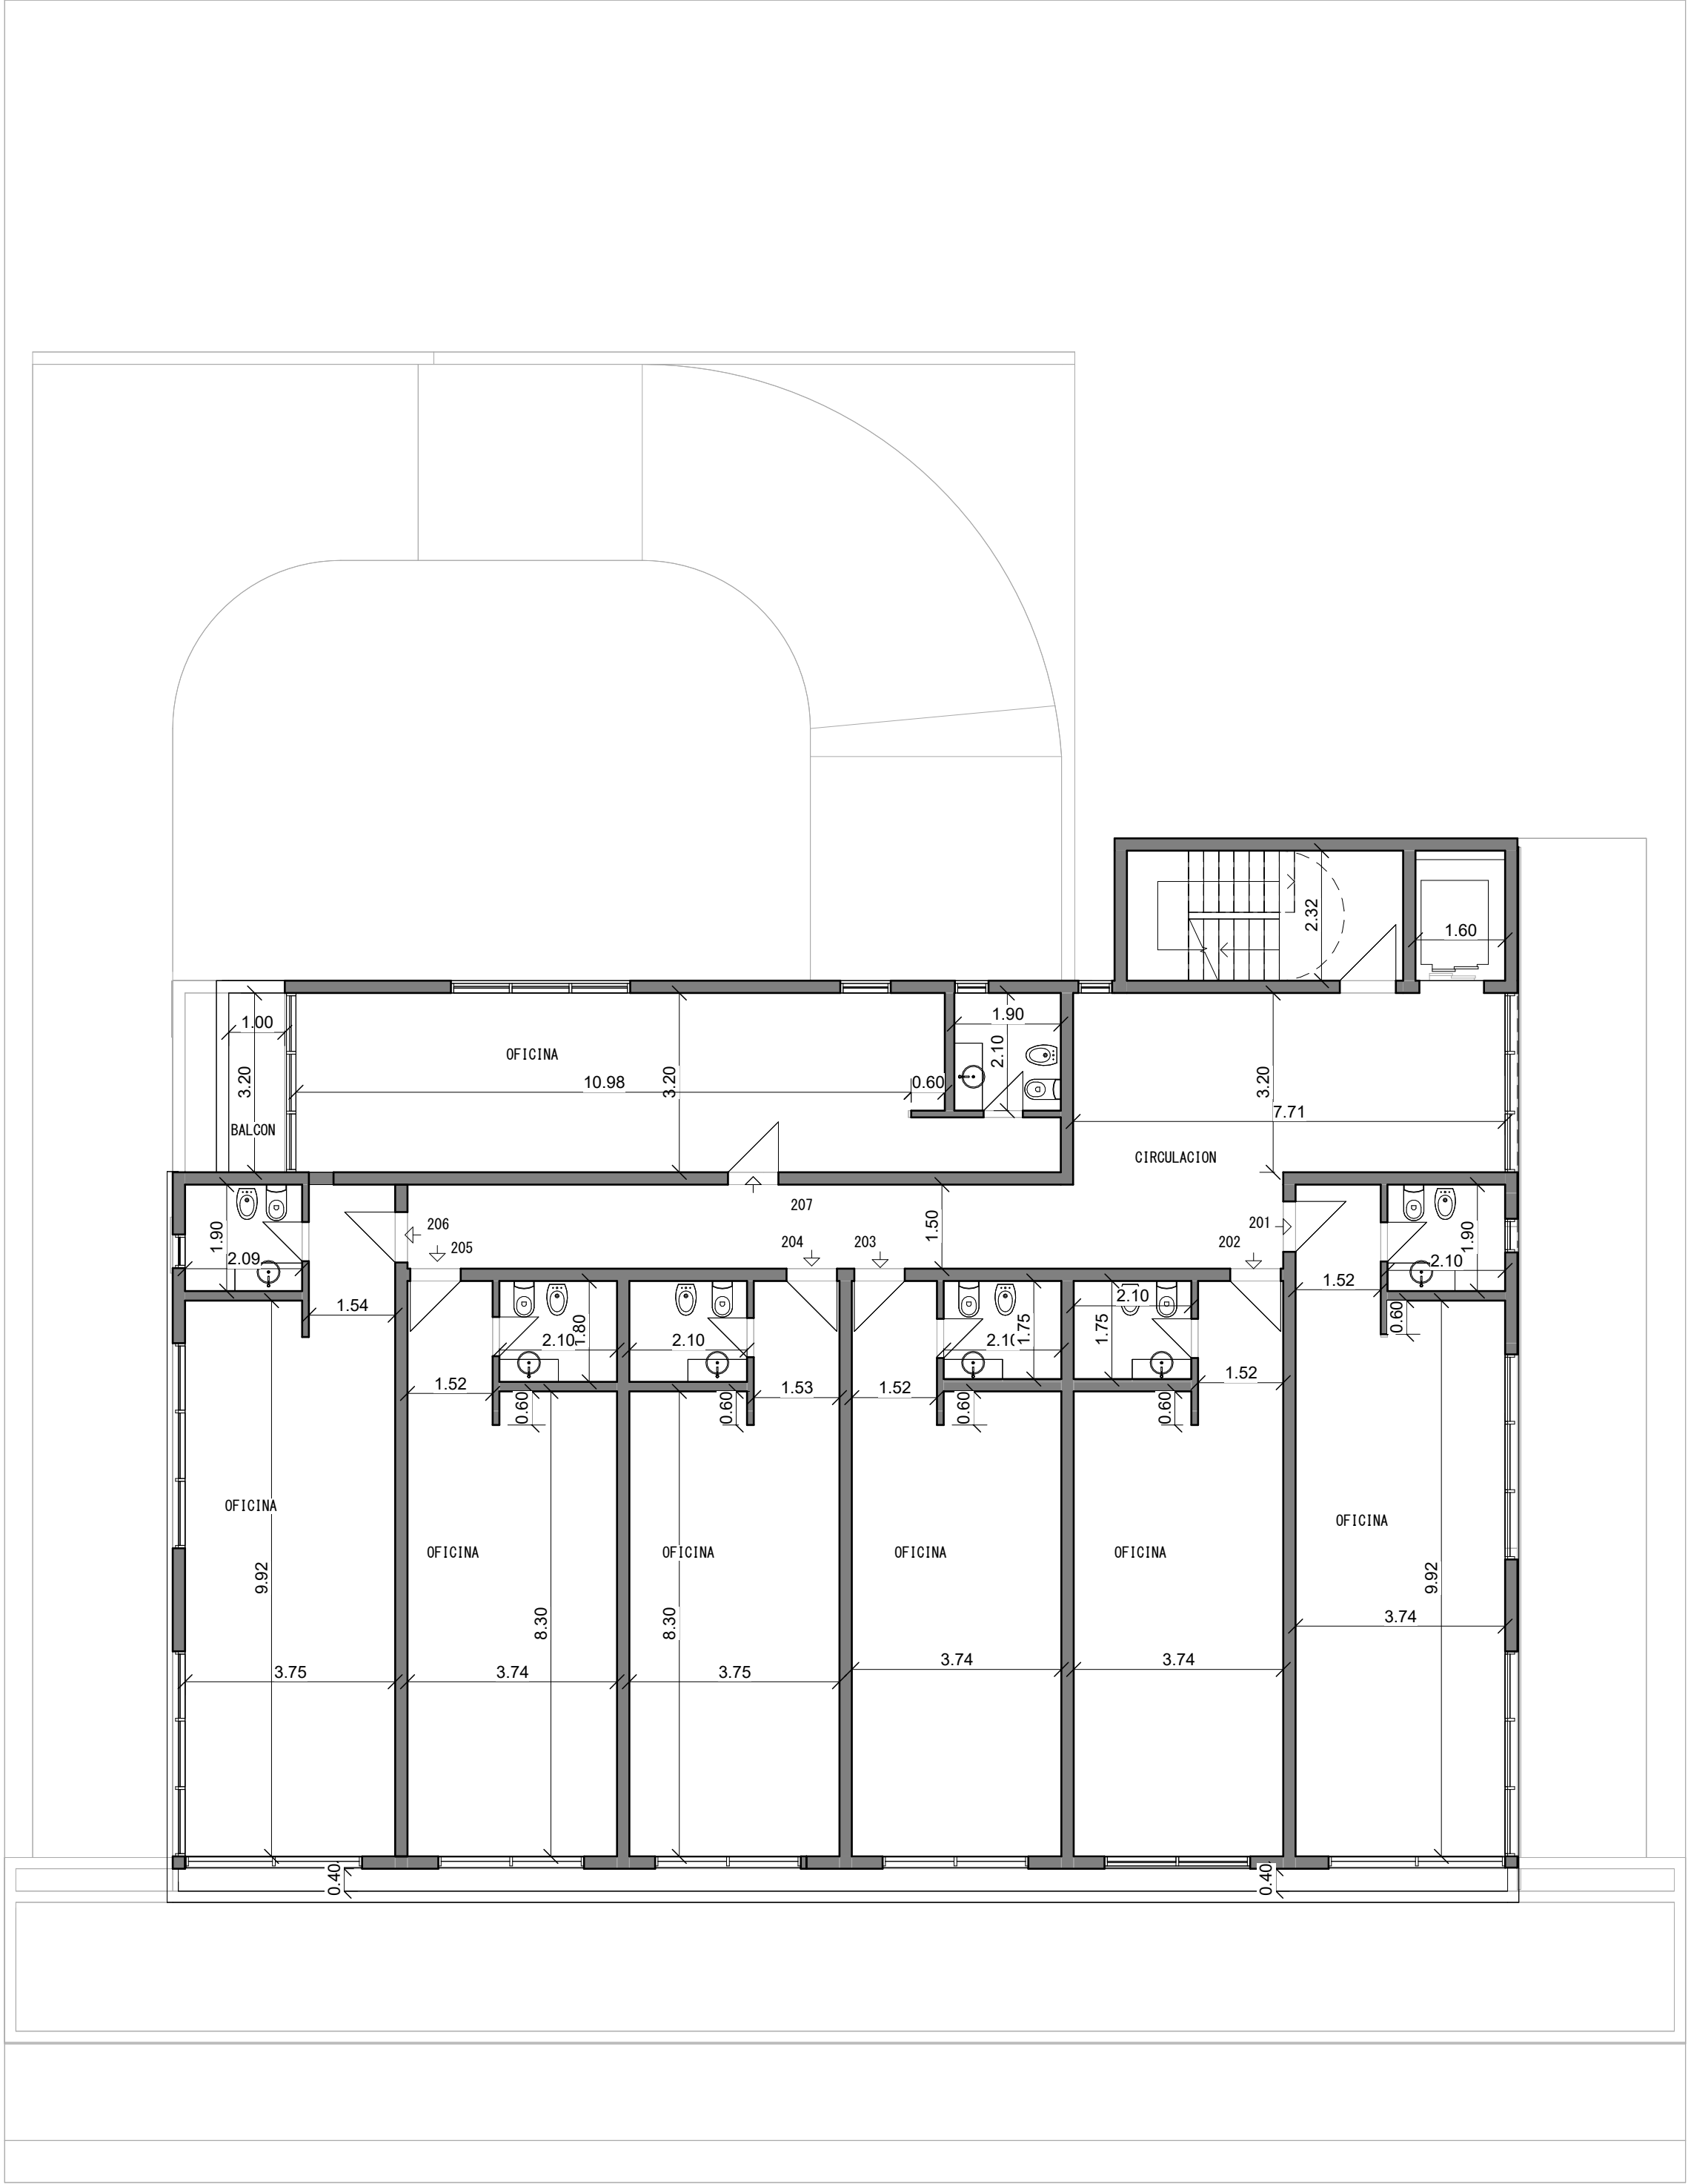

1 Piso 2
L05 1 : 100

OBRA SANTOS CHOQUE
2 lotes


Plano
PISO 2

L05

Fecha
04 JUNIO 2026


Escala
1 : 100

fmaarquitecto
2236 210 707 - (7167) Pinamar - Buenos Aires
fmaarquitecto23@gmail.com

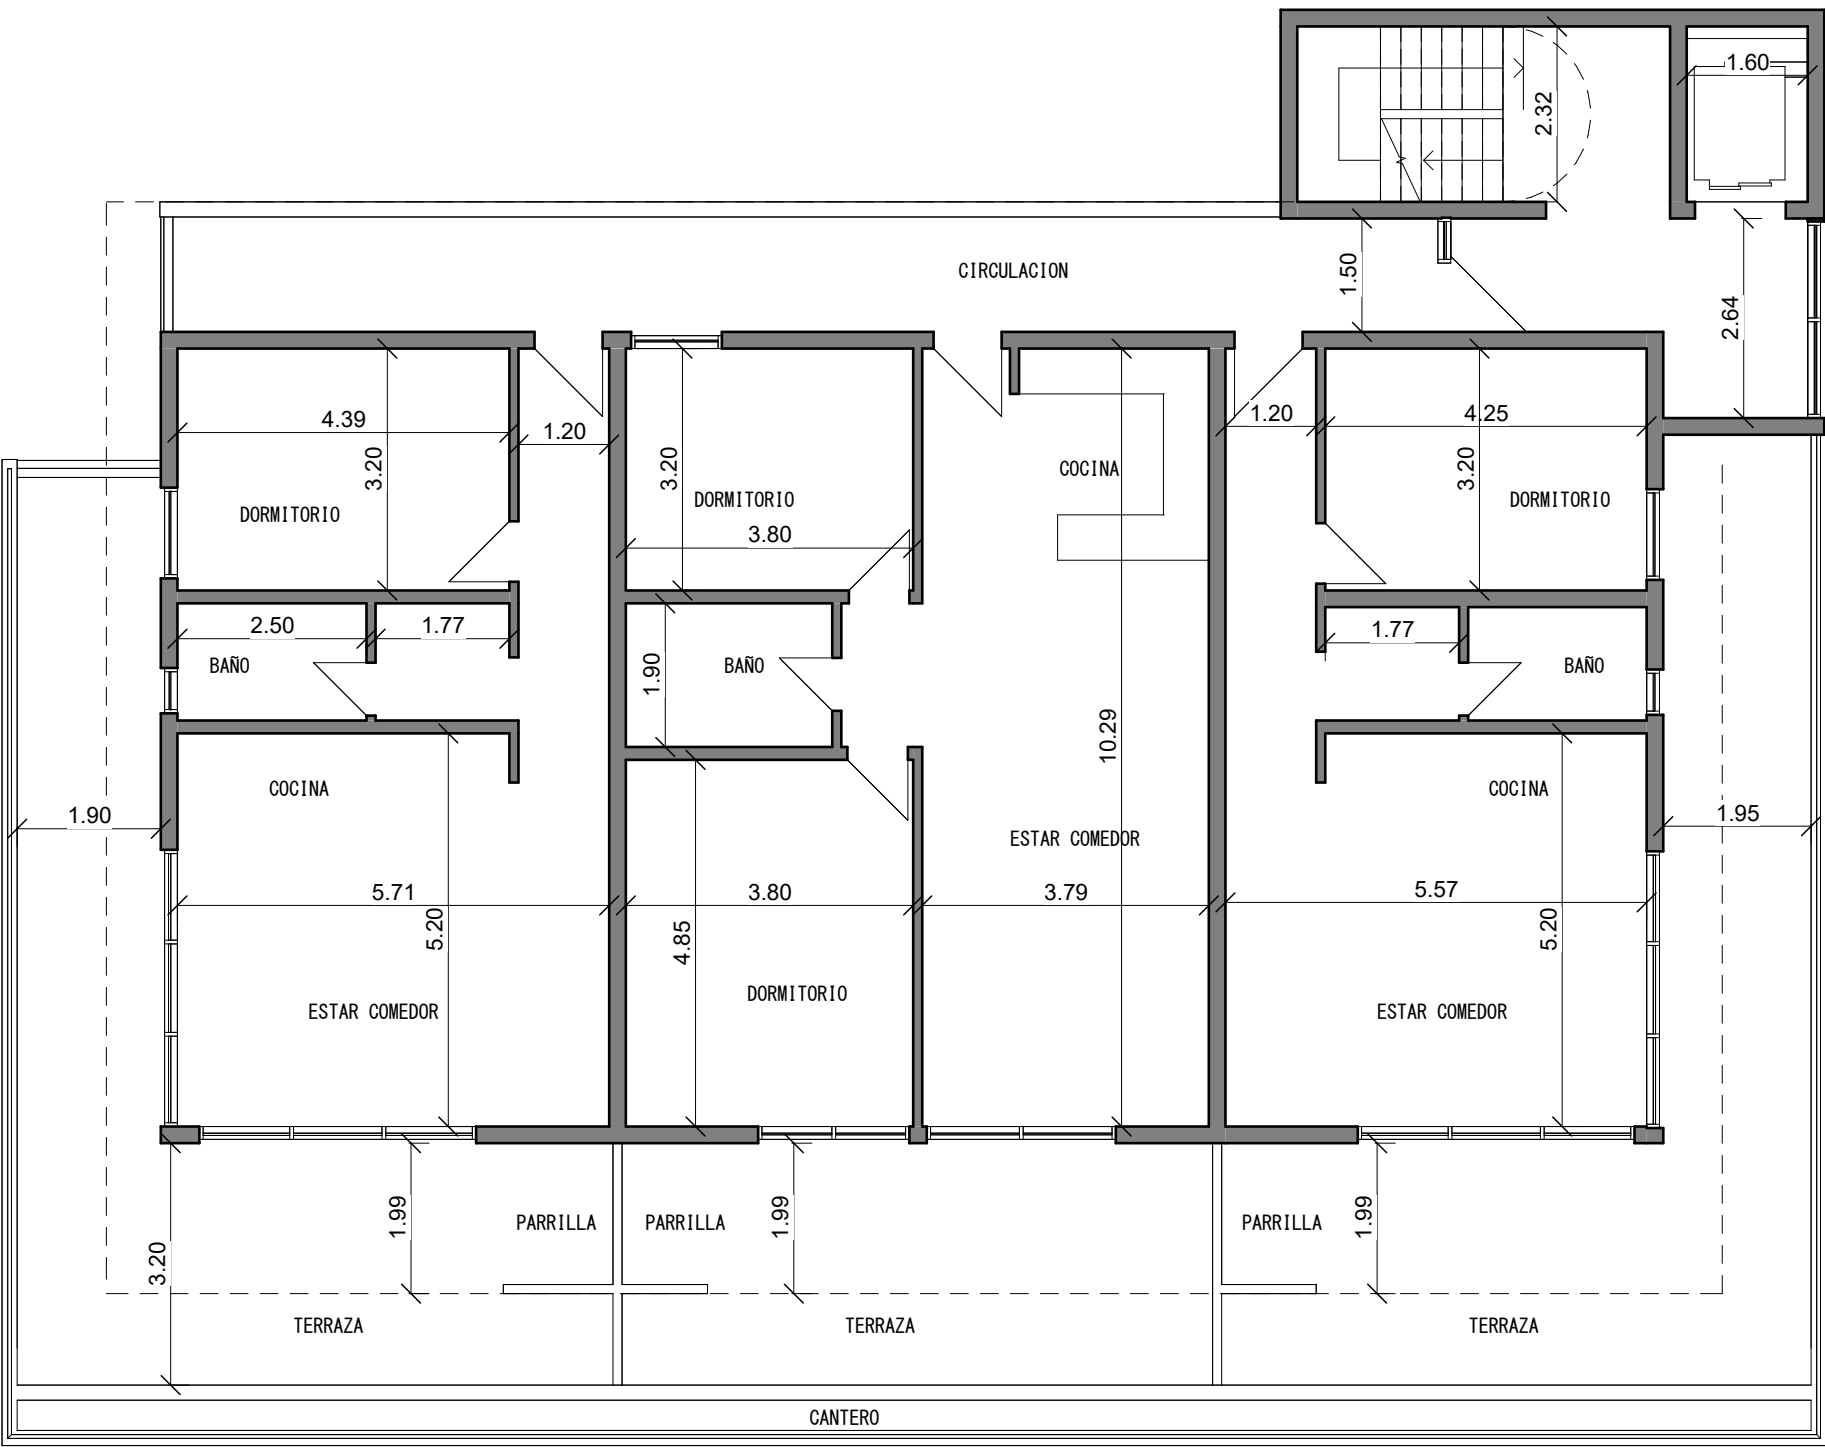


1
L06


Piso 3
1 : 100

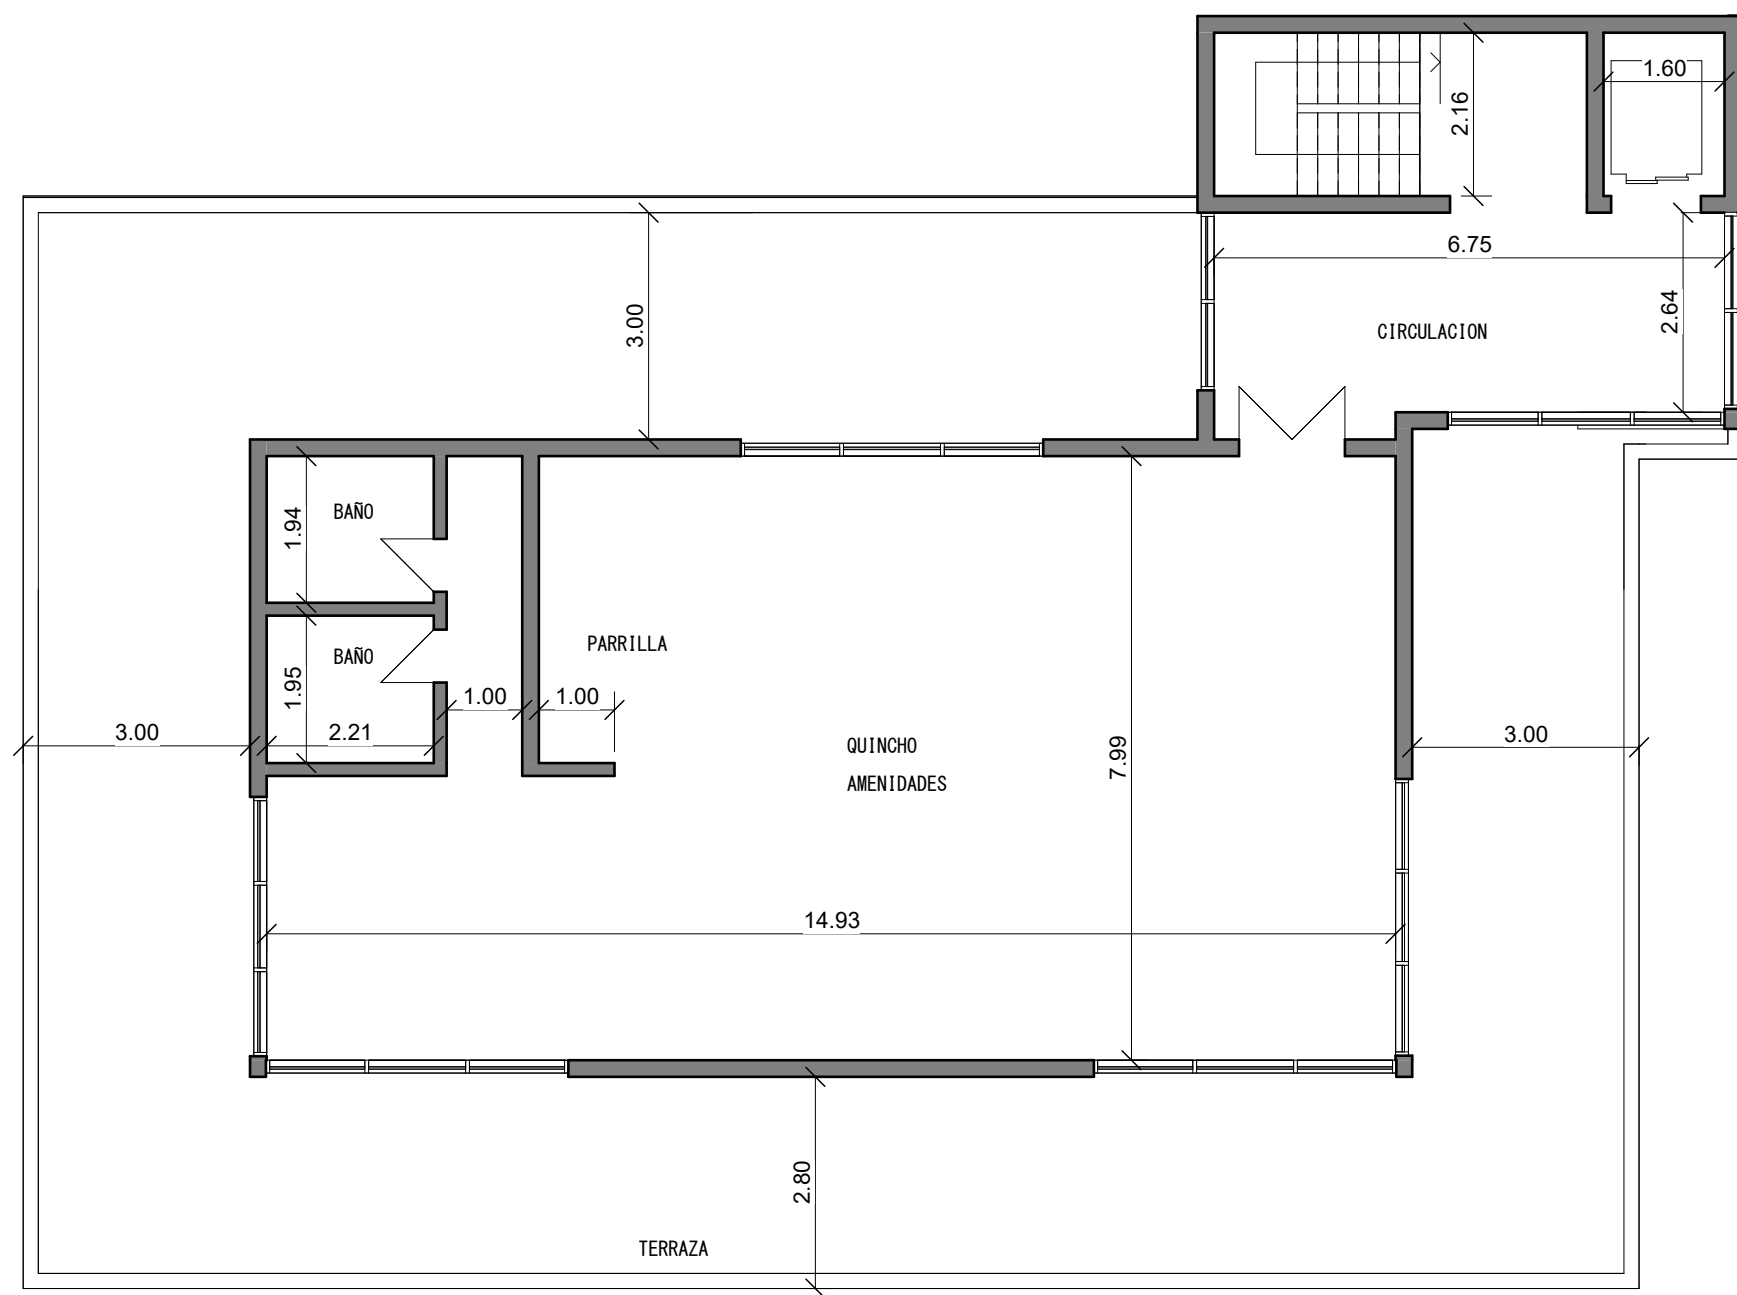

3	Piso 4
L07	1 : 100

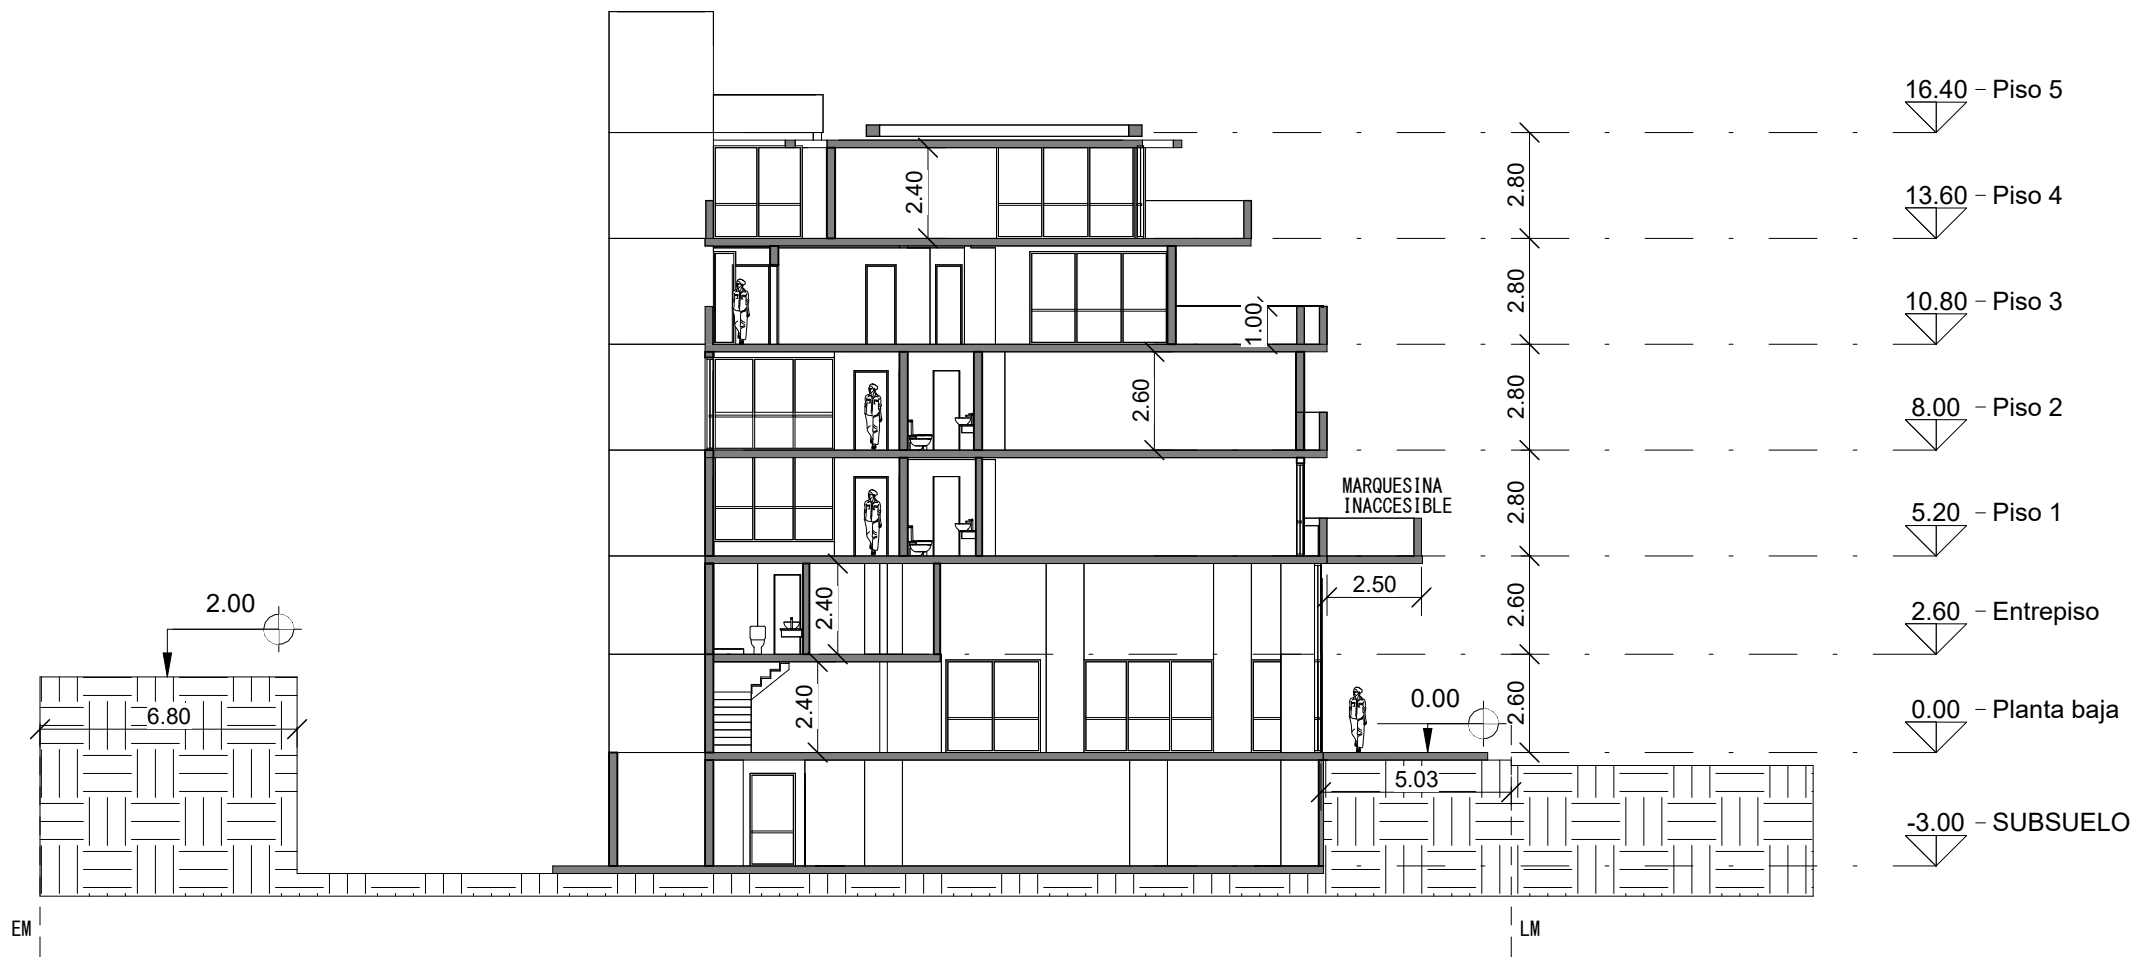

1 Sección 1
L08 1 : 200

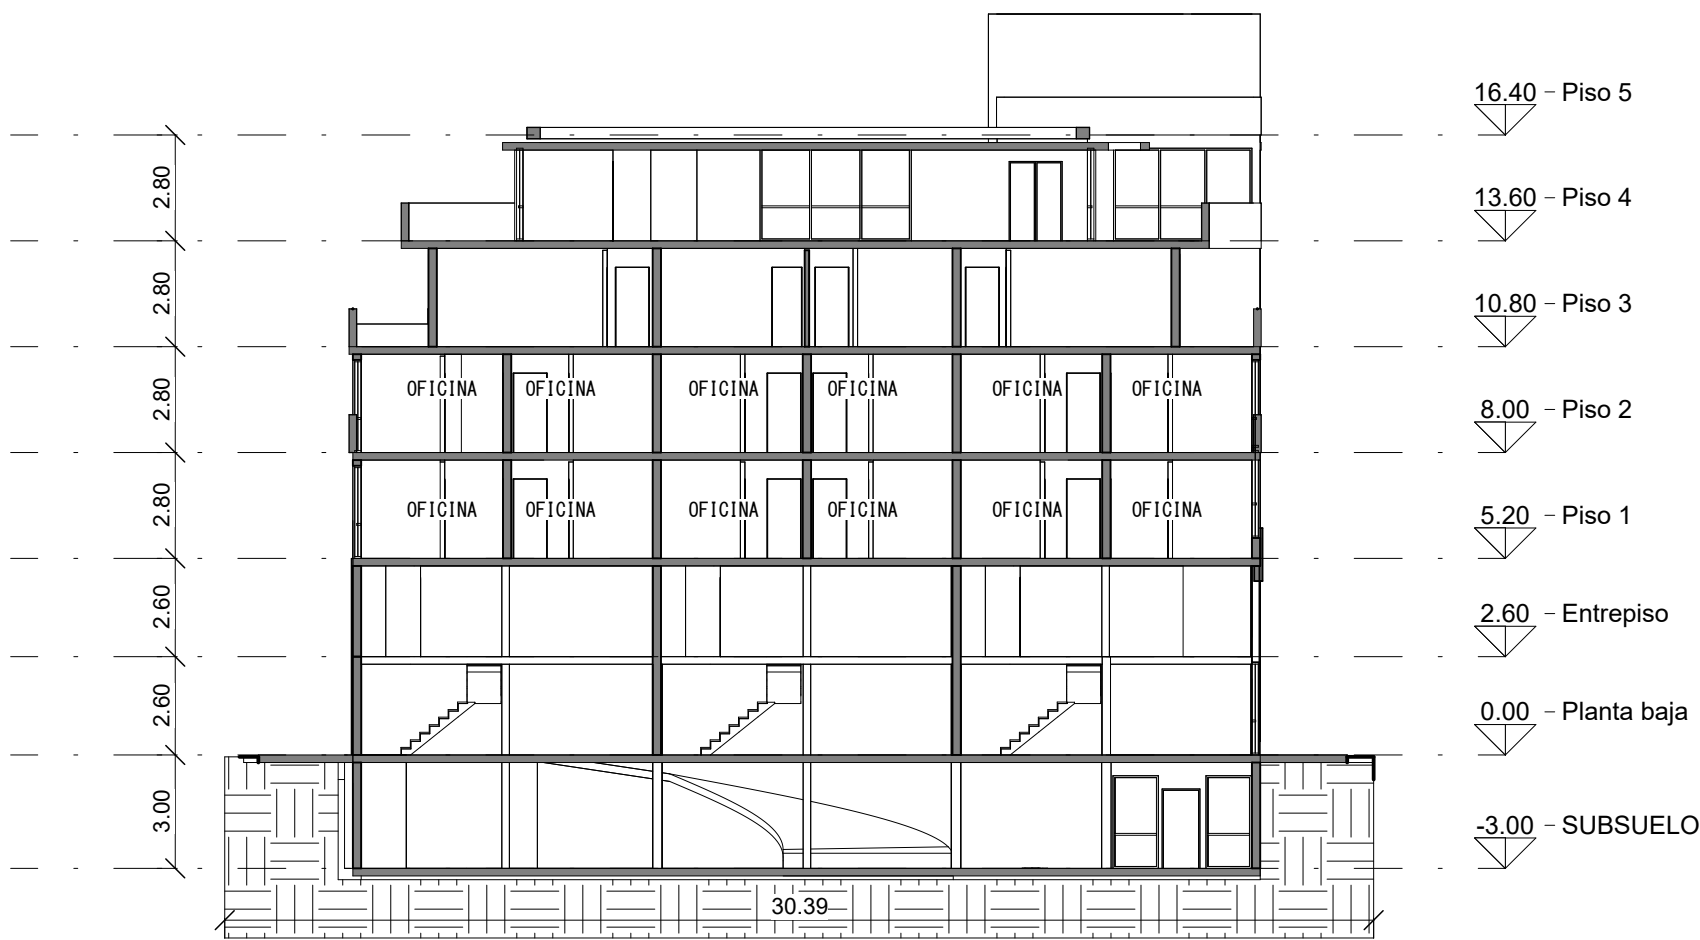

2 Sección 2
L08 1 : 200